


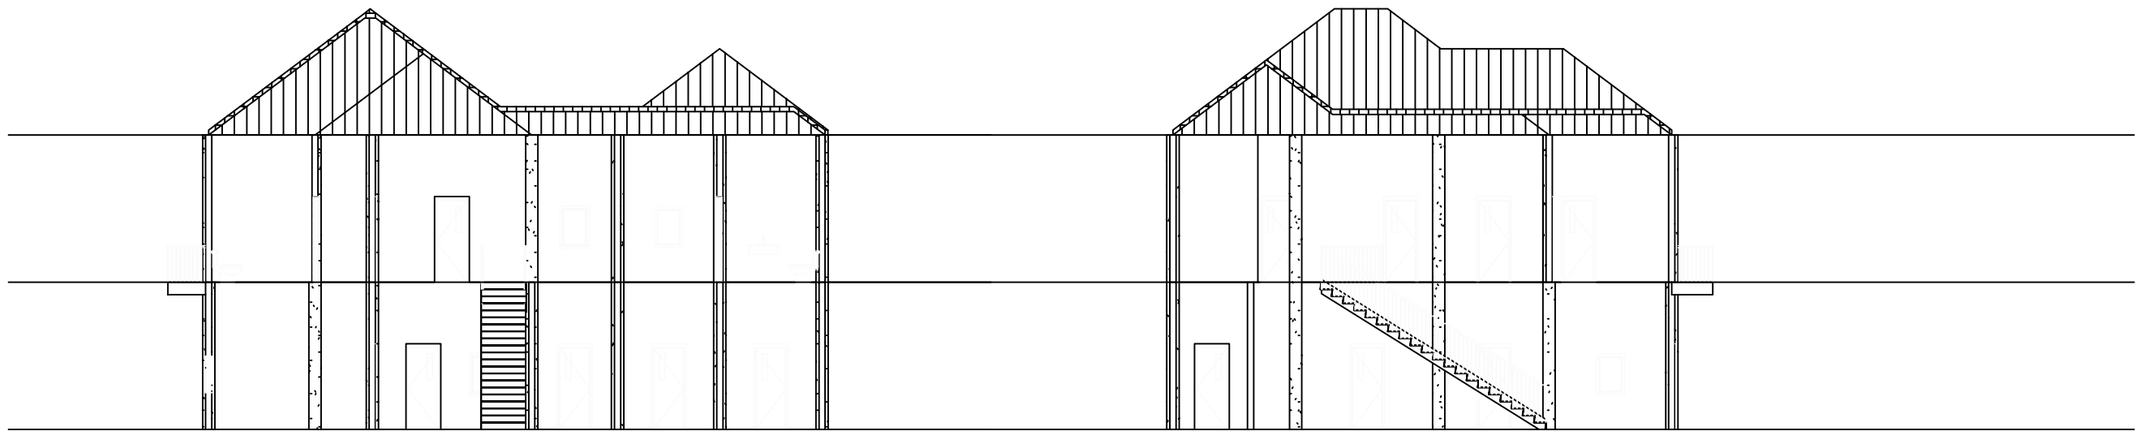


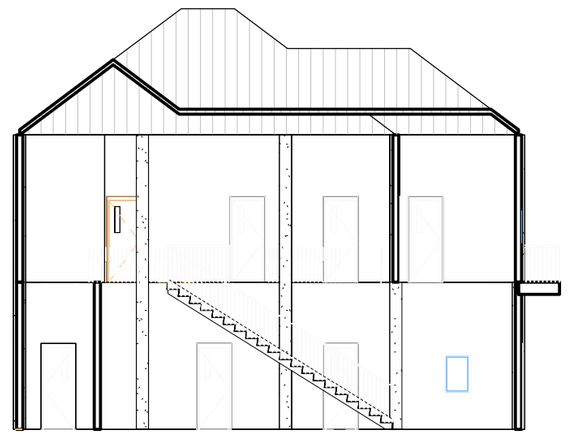


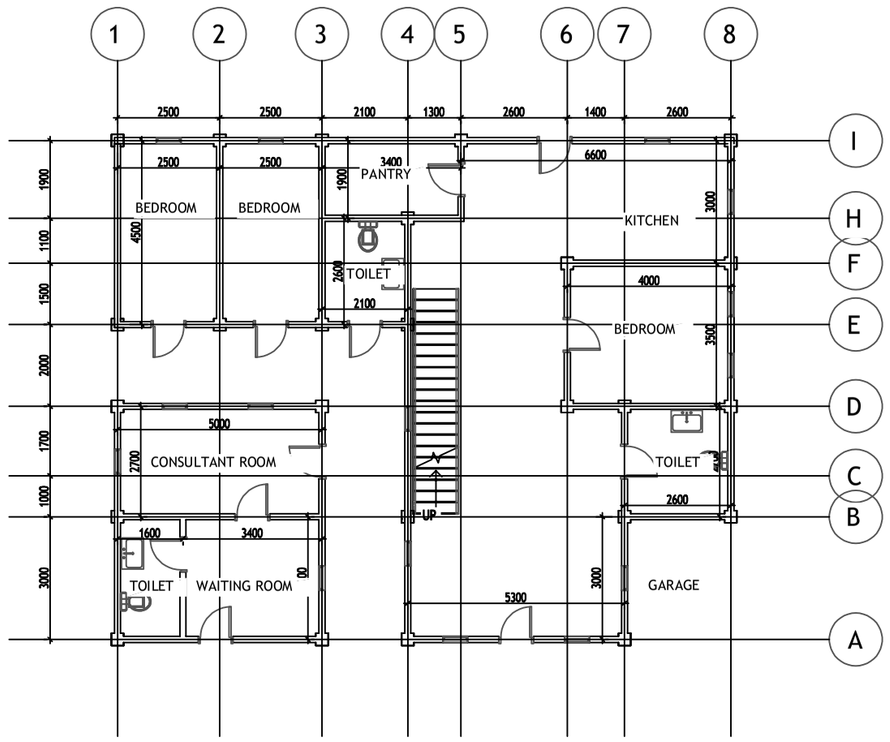


GROUND FLOOR PLAN

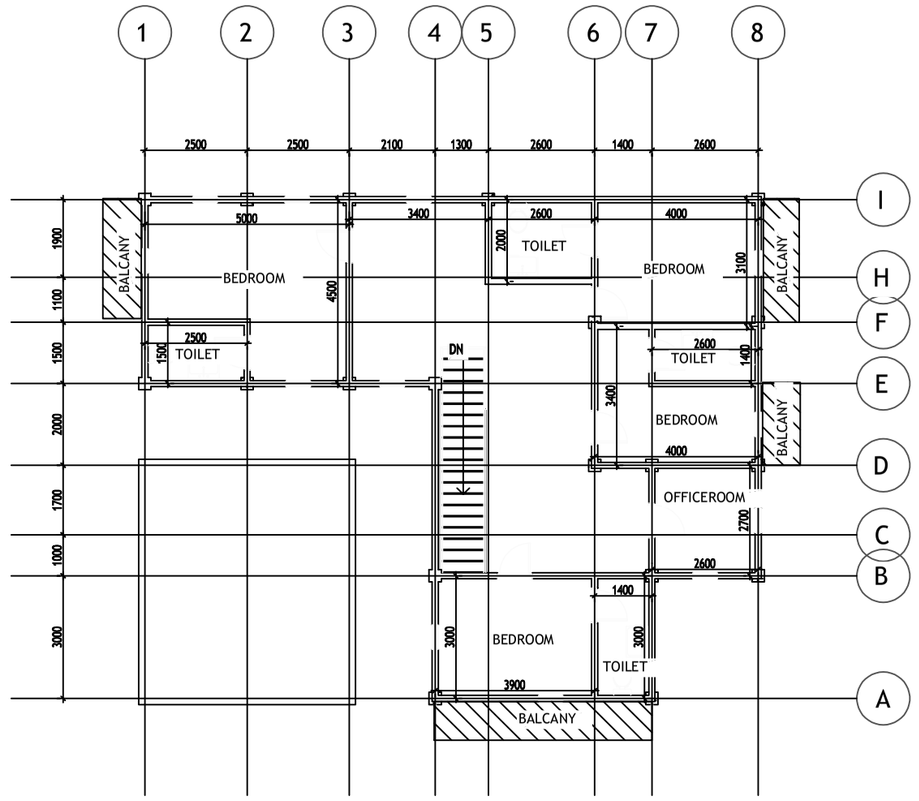


FIRST FLOOR PLAN

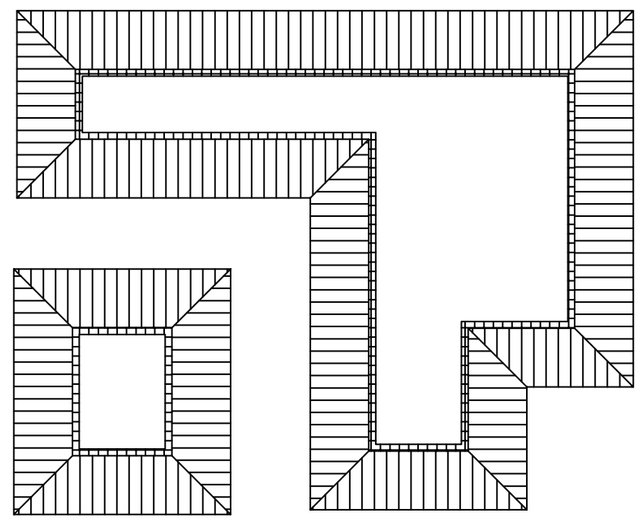


ROOF ARRANGEMENT

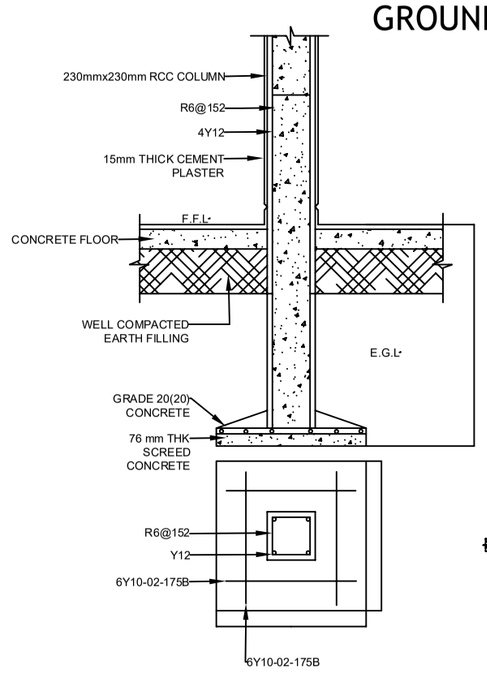


COLUMN DETAILS

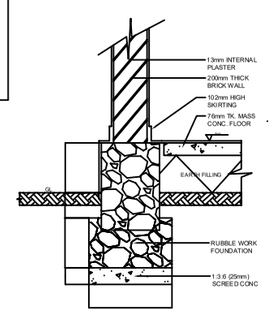


WALL FOUNDATION

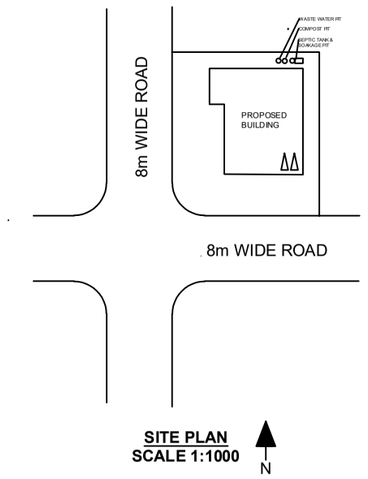

SITE PLAN
SCALE 1:1000

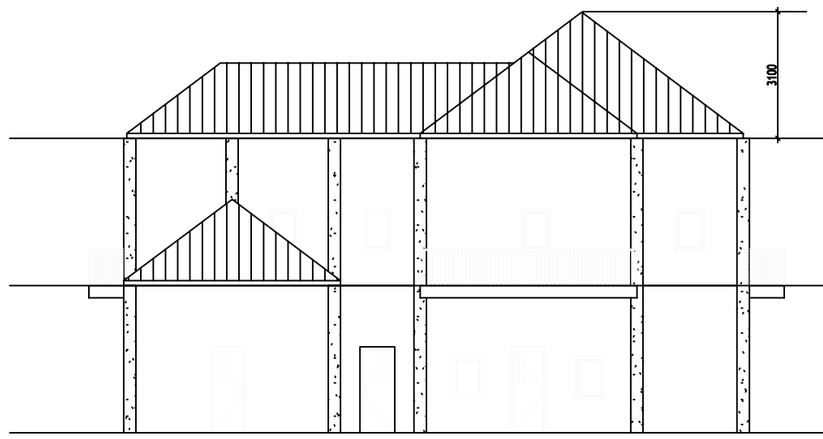

SOUTH ELEVATION

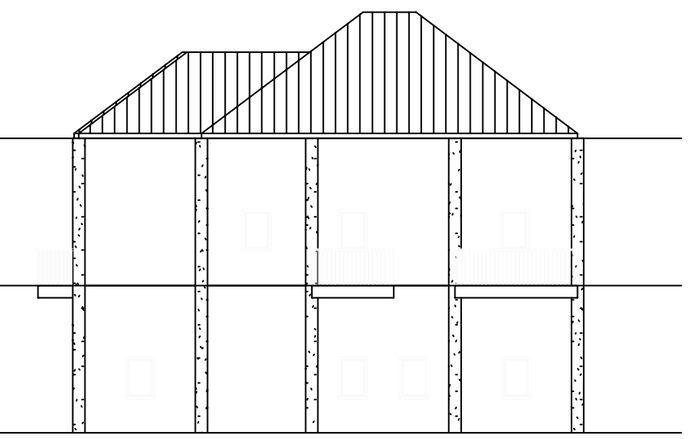

EAST ELEVATION

COUNCIL DRAWING

ALL DIMENSIONS ARE IN MILIMETRES

SCALE 1:150

DRG. NO. 1

NAME: AATHITHTHAN S.

REG. NO.: E/22/037

DATE: 20/07/2026